
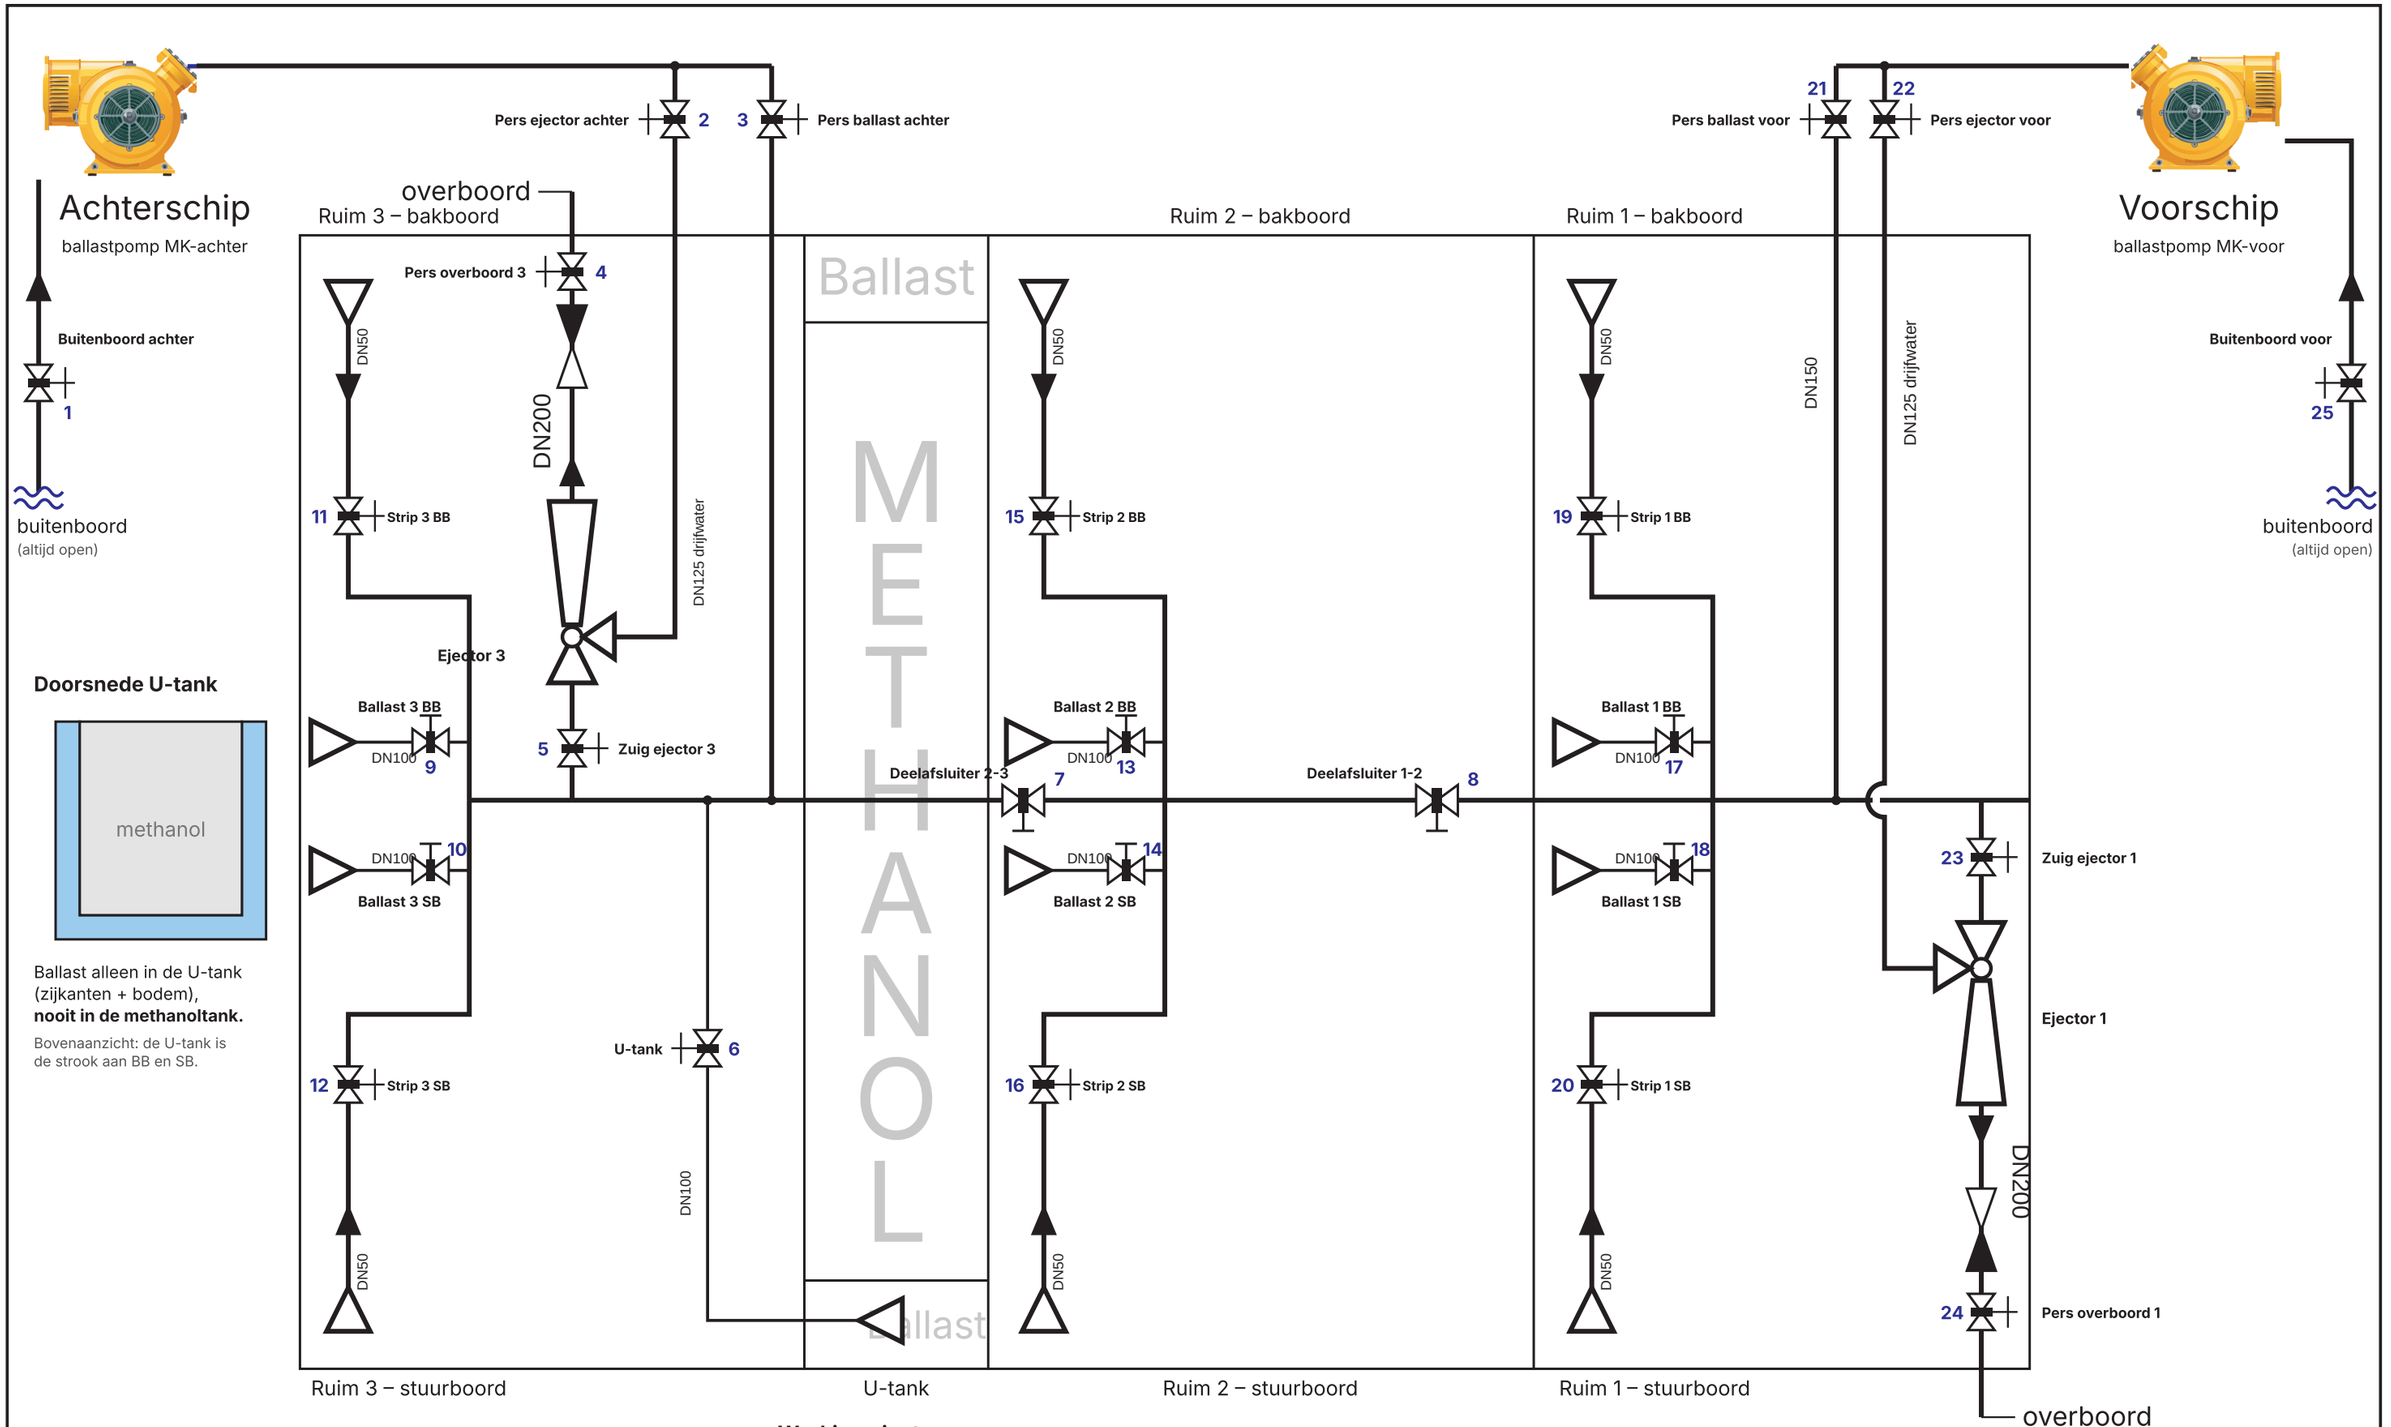


Doorsnede U-tank

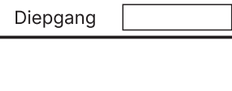

Ballast alleen in de U-tank (zijkanten + bodem), **nooit in de methanoltank.**


Bovenaanzicht: de U-tank is de strook aan BB en SB.

Peilgegevens (uit scheepsprofiel – leeg = nog invullen)

	Alarm	Max.	Doelpeil
Ruim 3			
U-tank			
Ruim 2			
Ruim 1			

Diepgang ____ Sygo ____ Zaadhout 140 cm

Werking ejector

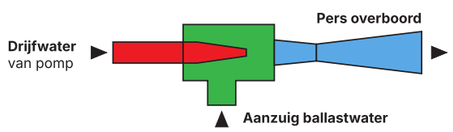

Drijfwater zuigt via onderdruk het ballastwater mee.

Legenda

- Afsluiter open (O)
- Afsluiter dicht (D)
- Zuigmond in ruim
- Terugslagklep
- Ballastwater

Ballastsysteem S-serie

Controleblad

S-serie	versie 2.2 (concept)
groen = open · rood = dicht	rust: dicht · buitenboord open

Controleblad – Ballastsysteem S-serie

Loop elke afsluiter na (nummer = nummer op blad 1). Vink aan of de plek klopt en schrijf de naam op zoals hij aan boord heet, als die anders is.

Nr	Afsluiter in de simulator	Plek klopt	Naam aan boord (als anders)	Opmerking
1	Buitenboord achter	☐ ja ☐ nee		
2	Pers ejector achter	☐ ja ☐ nee		
3	Pers ballast achter	☐ ja ☐ nee		
4	Pers overboord 3	☐ ja ☐ nee		
5	Zuig ejector 3	☐ ja ☐ nee		
6	U-tank	☐ ja ☐ nee		
7	Deelafsluiter 2-3	☐ ja ☐ nee		
8	Deelafsluiter 1-2	☐ ja ☐ nee		
9	Ballast 3 BB	☐ ja ☐ nee		
10	Ballast 3 SB	☐ ja ☐ nee		
11	Strip 3 BB	☐ ja ☐ nee		
12	Strip 3 SB	☐ ja ☐ nee		
13	Ballast 2 BB	☐ ja ☐ nee		
14	Ballast 2 SB	☐ ja ☐ nee		
15	Strip 2 BB	☐ ja ☐ nee		
16	Strip 2 SB	☐ ja ☐ nee		
17	Ballast 1 BB	☐ ja ☐ nee		
18	Ballast 1 SB	☐ ja ☐ nee		
19	Strip 1 BB	☐ ja ☐ nee		
20	Strip 1 SB	☐ ja ☐ nee		
21	Pers ballast voor	☐ ja ☐ nee		
22	Pers ejector voor	☐ ja ☐ nee		
23	Zuig ejector 1	☐ ja ☐ nee		
24	Pers overboord 1	☐ ja ☐ nee		
25	Buitenboord voor	☐ ja ☐ nee		

Open vragen

1. U-tank: is het één leiding voor vullen én zuigen? Maat (DN): _____ Drainleiding aanwezig? ☐ ja ☐ nee – waar / welke afsluiter: _____
2. Buitenboord: heeft elke machinekamer één buitenboordafsluiter voor de ballastpomp? ☐ ja ☐ nee – naam aan boord: _____
3. DN-maten: Pers ballast achter _____ · voor DN150? _____ · drijfwater DN125? _____ · overboord DN200? _____ · zuigmonden DN100? _____ · strips DN50? _____
4. Stripleidingen: BB voor en SB achter in elk ruim? ☐ ja ☐ nee – opmerking: _____
5. Ontbreekt er iets op het schema (afsluiter, leiding, peilbuis)? _____

Scheepsgegevens

	Hoogwateralarm	Max. niveau	Doelpeil
Ruim 3	_____	_____	_____
U-tank	_____	_____	_____
Ruim 2	_____	_____	_____
Ruim 1	_____	_____	_____

Zaadhout: 140 cm U-tank inhoud: _____ t

Omschrijving	Diepgang	Sygo-stand

Pompcapaciteit: _____ m³/h Ejector: _____ m³/h

Gecontroleerd door: _____ Datum: _____ Schip: _____